


Схема расположения стоек

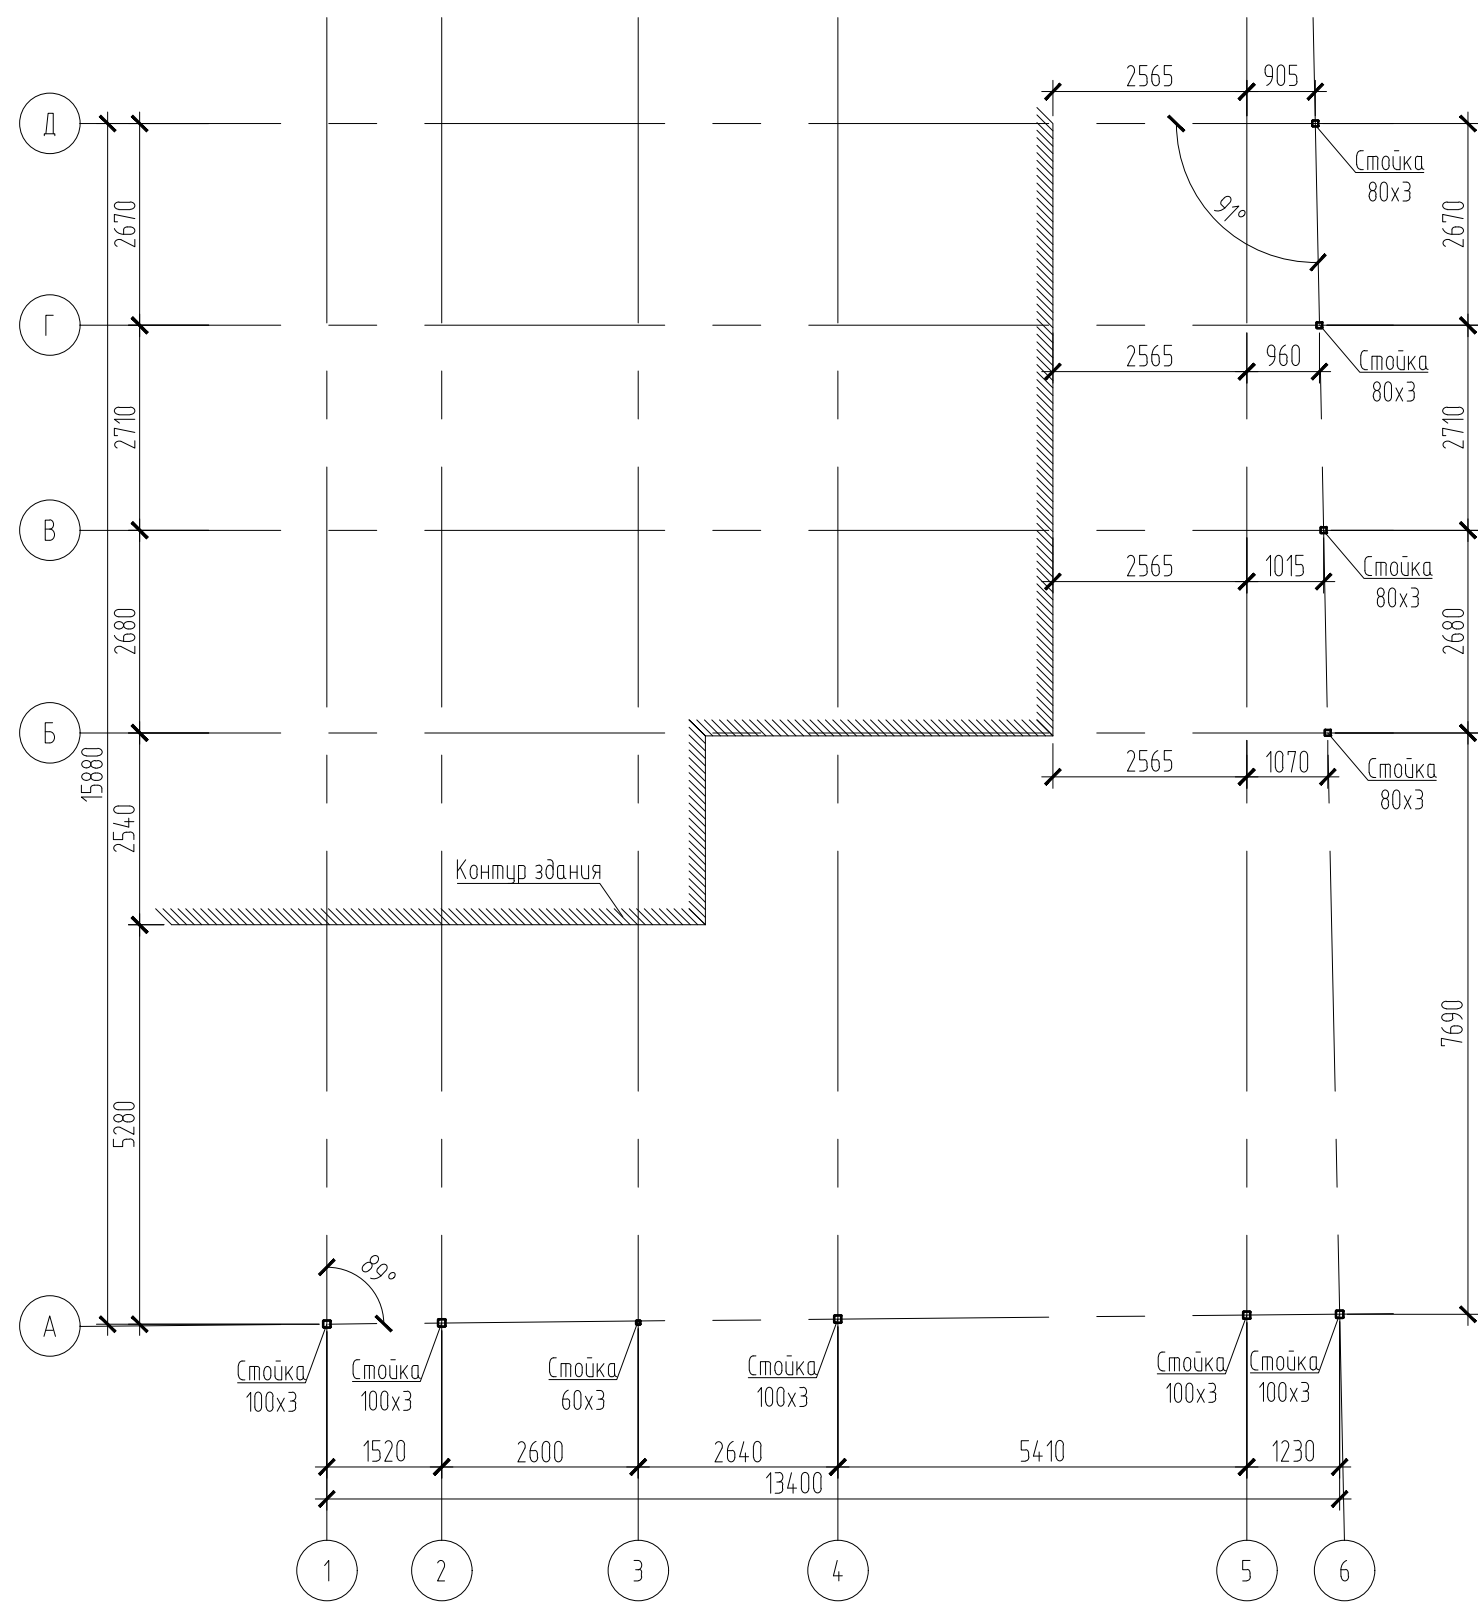

Согласовано:


Взам. инв. №

Подп. и дата

Инв. № подл.

						1			
						1			
Изм.	Кол.уч.	Лист	№ док.	Подп.	Дата	1	Стадия	Лист	Листов
Разработал					05.24		Р	1	
ГИП					05.24	Схема расположения стоек			
Н.контроль					05.24				

Схема расположения стальных ферм покрытия

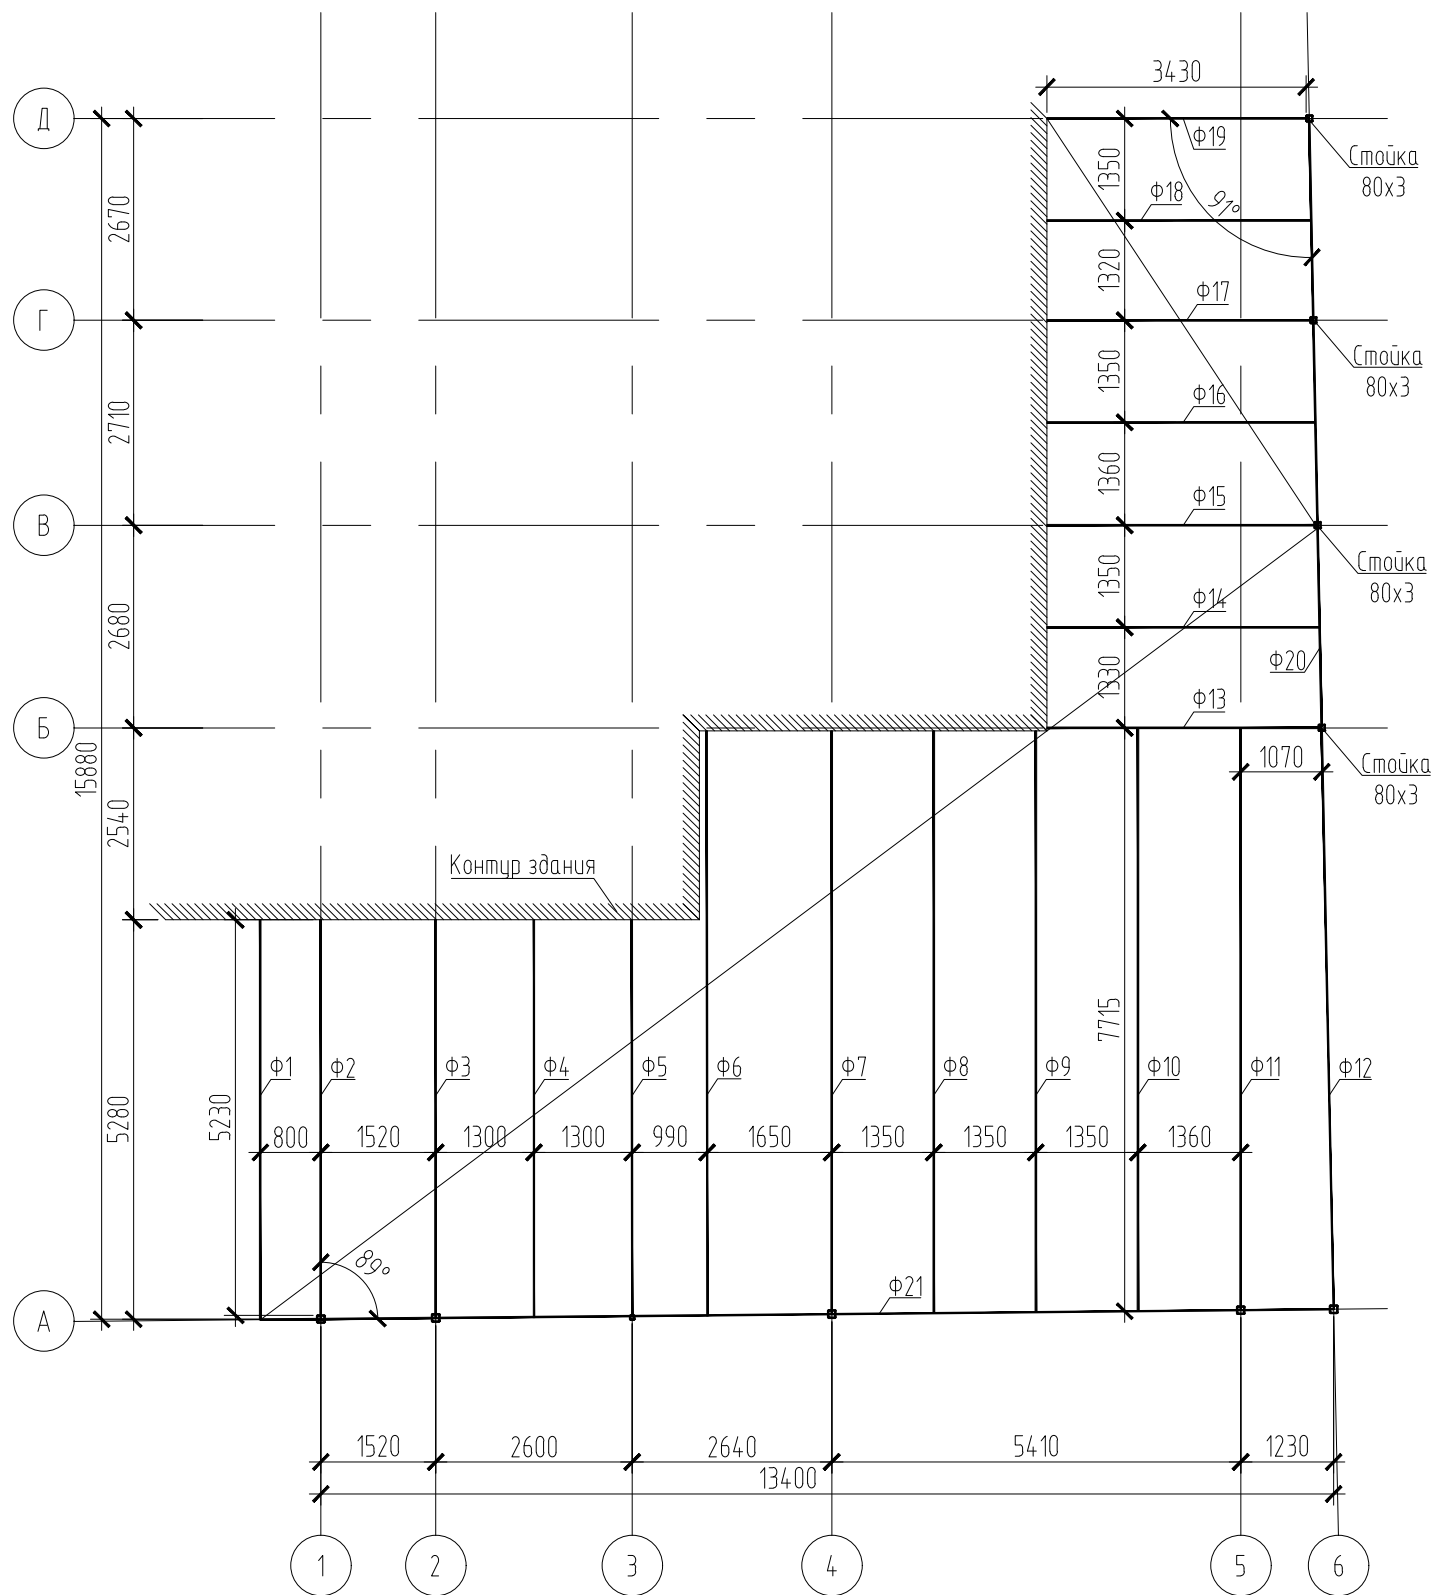


Согласовано:			

Взам. инв. №	
Подп. и дата	
Инв. № подл.	

						1			
						1			
Изм.	Кол.уч.	Лист	№ док.	Подп.	Дата	1	Стадия	Лист	Листов
Разработал					05.24		Р	2	
ГИП					05.24	Схема расположения стальных ферм покрытия			
Н.контроль					05.24				

Согласовано:


Взам. инб. №	
Подп. и дата	
Инб. № подл.	

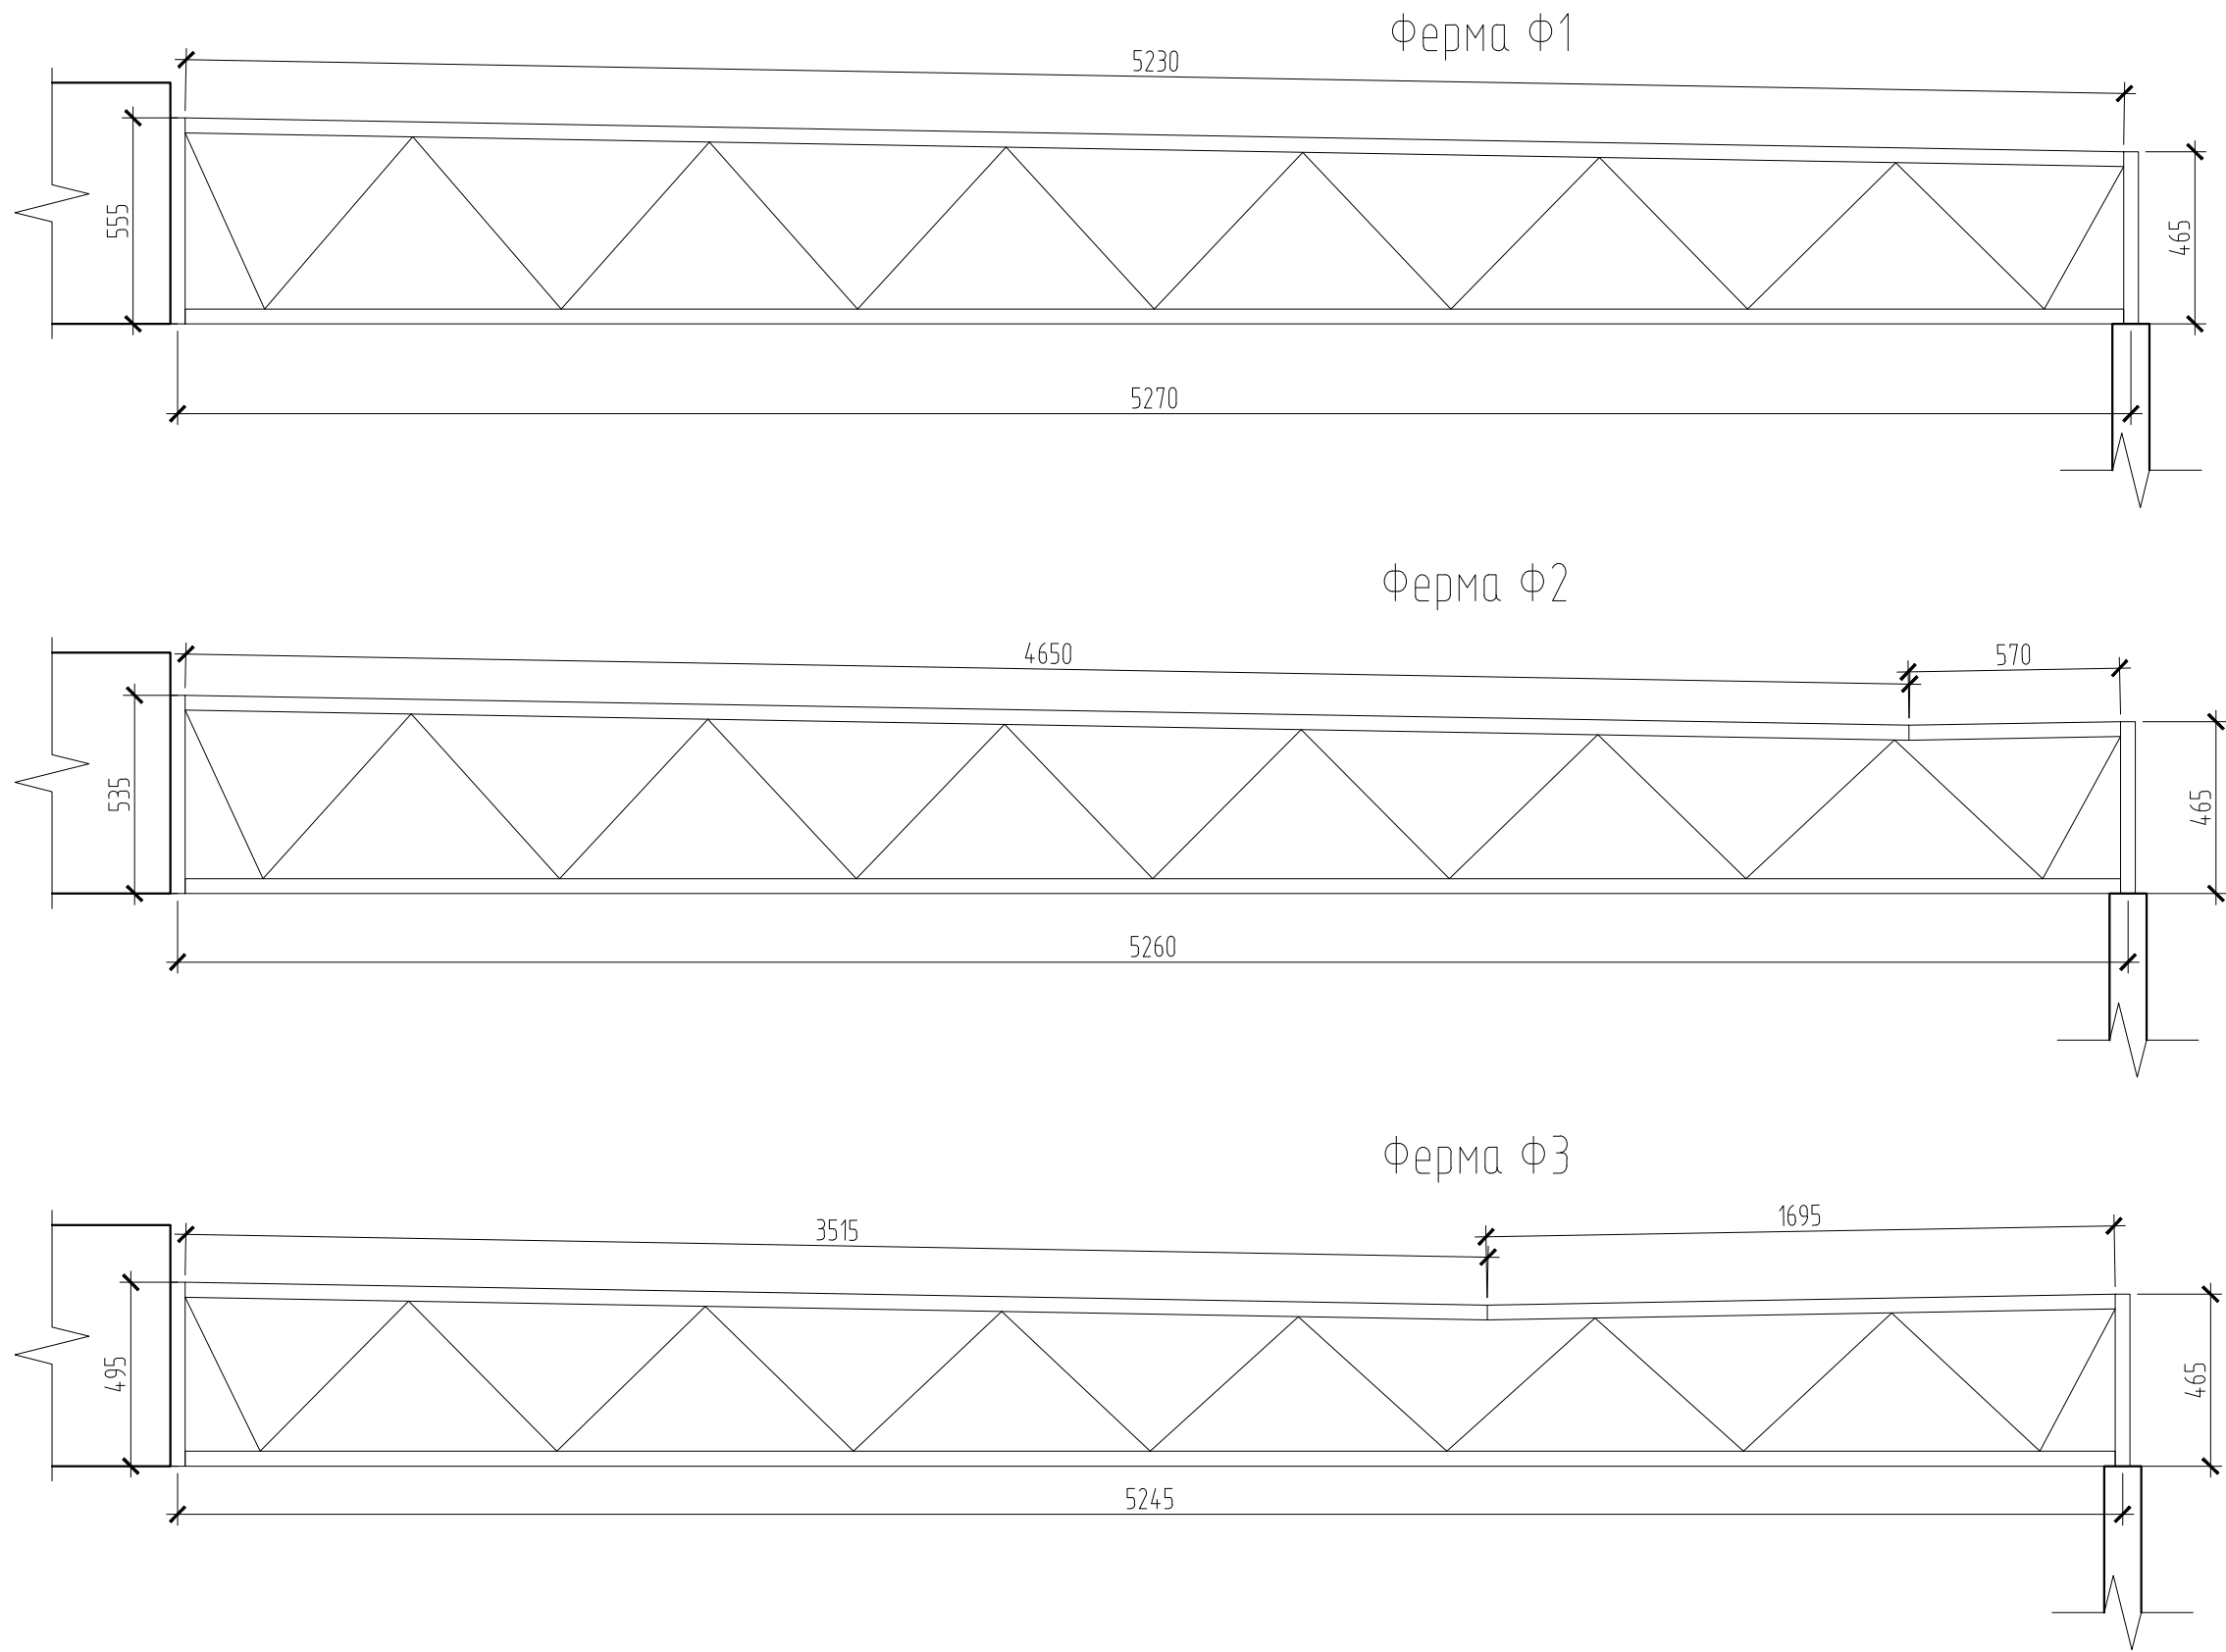

						1			
						1			
Изм.	Кол.уч.	Лист	№ док.	Подп.	Дата	1	Стадия	Лист	Листов
Разработал					05.24		Р	3	
ГИП					05.24	Фермы Ф1, Ф2, Ф3	1		
Н.контроль					05.24				




Согласовано:

Взам. инб. №	
Подп. и дата	
Инб. № подл.	

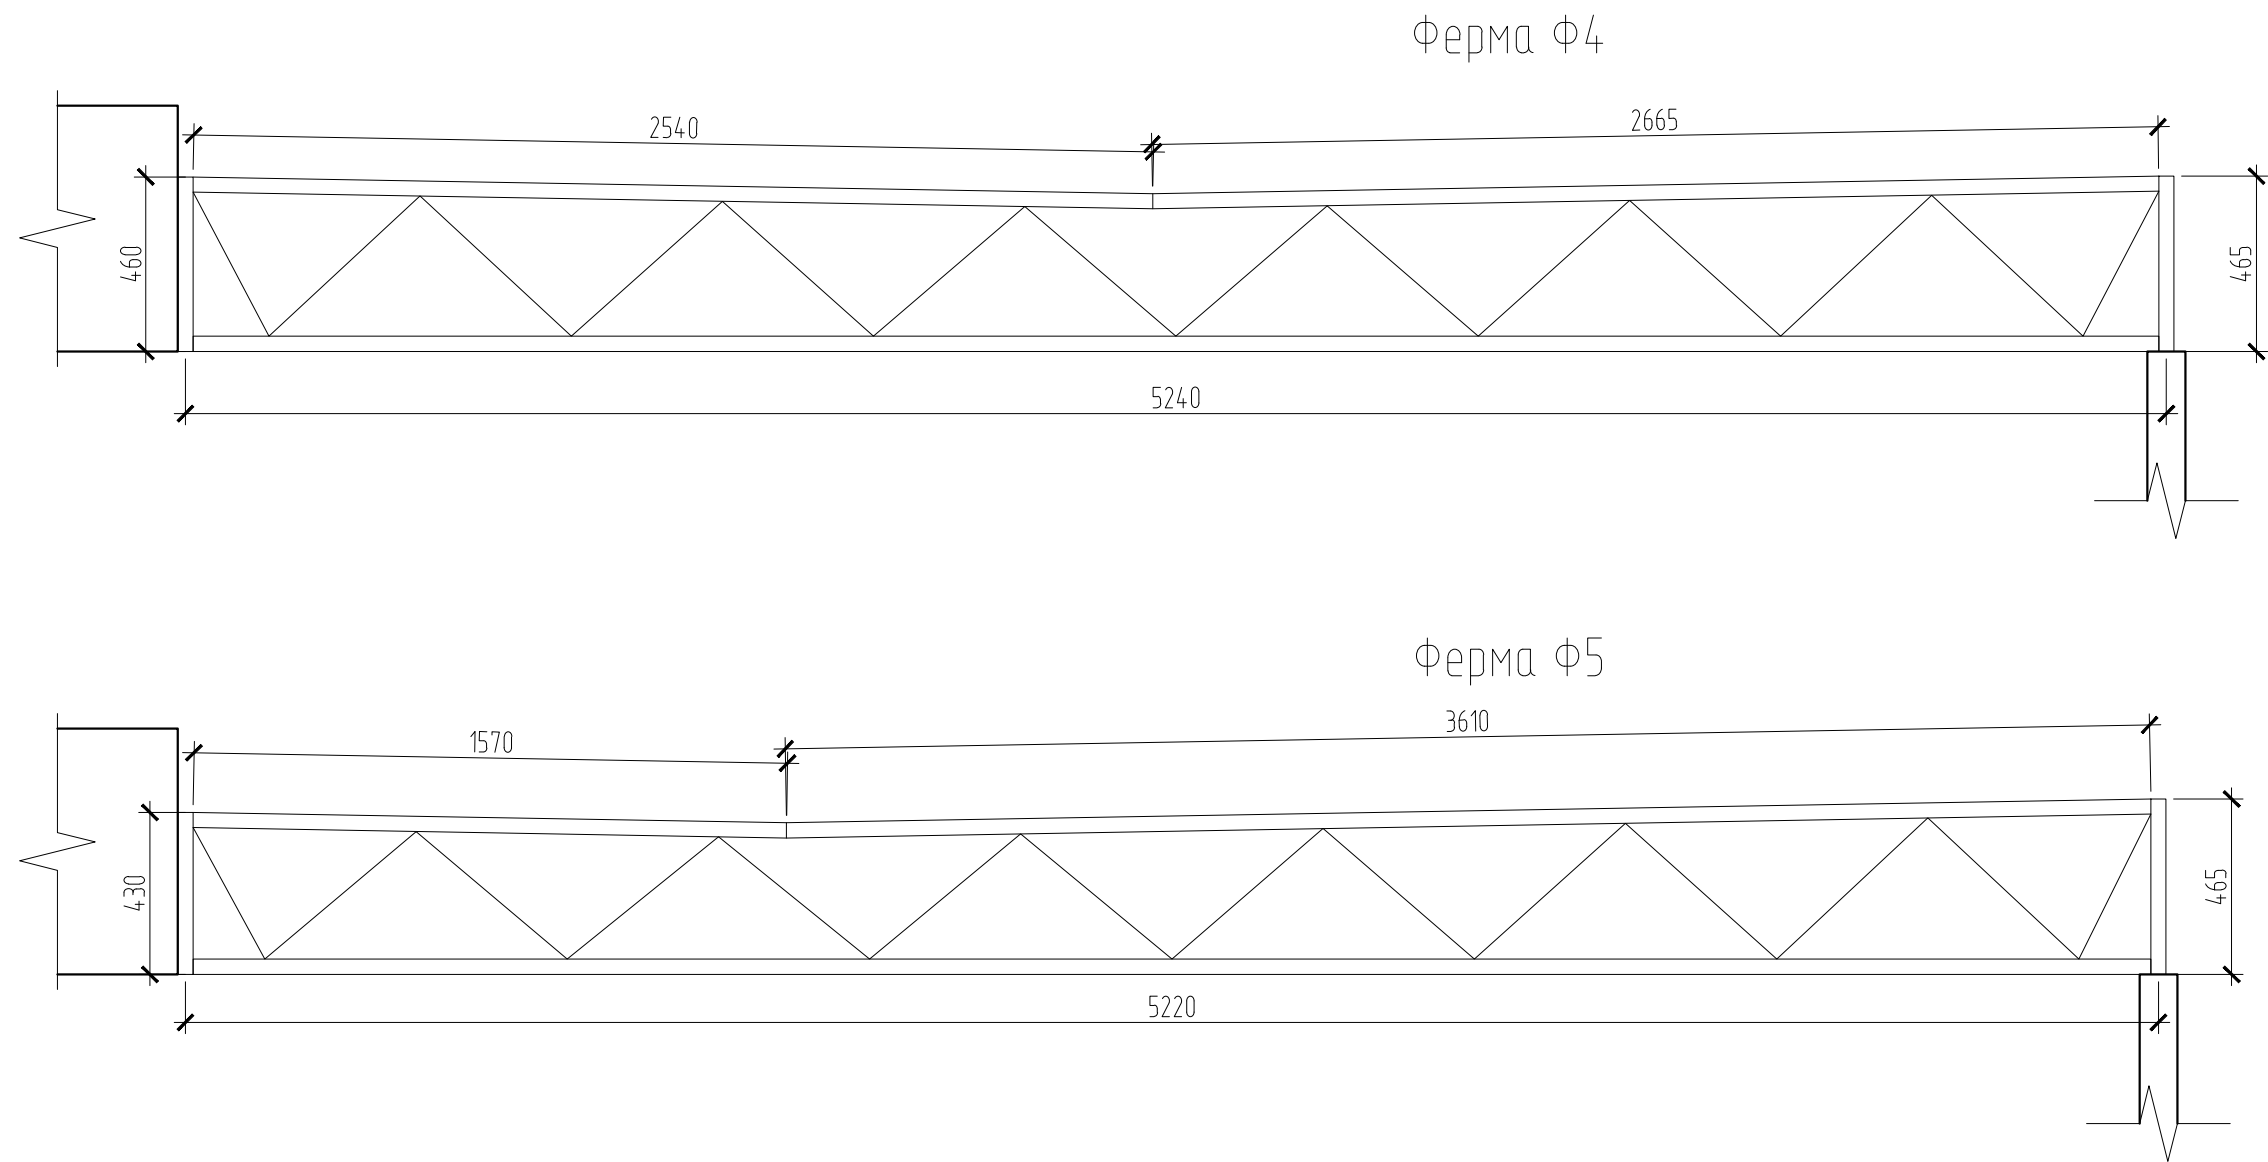


						1			
						1			
Изм.	Кол.уч.	Лист	№ док.	Подп.	Дата	1	Стадия	Лист	Листов
Разработал					05.24		Р	4	
ГИП					05.24				
						Фермы Ф4, Ф5	1		
Н.контроль					05.24				

Согласовано:			
Взам. инб. №			
Подп. и дата			
Инб. № подл.			

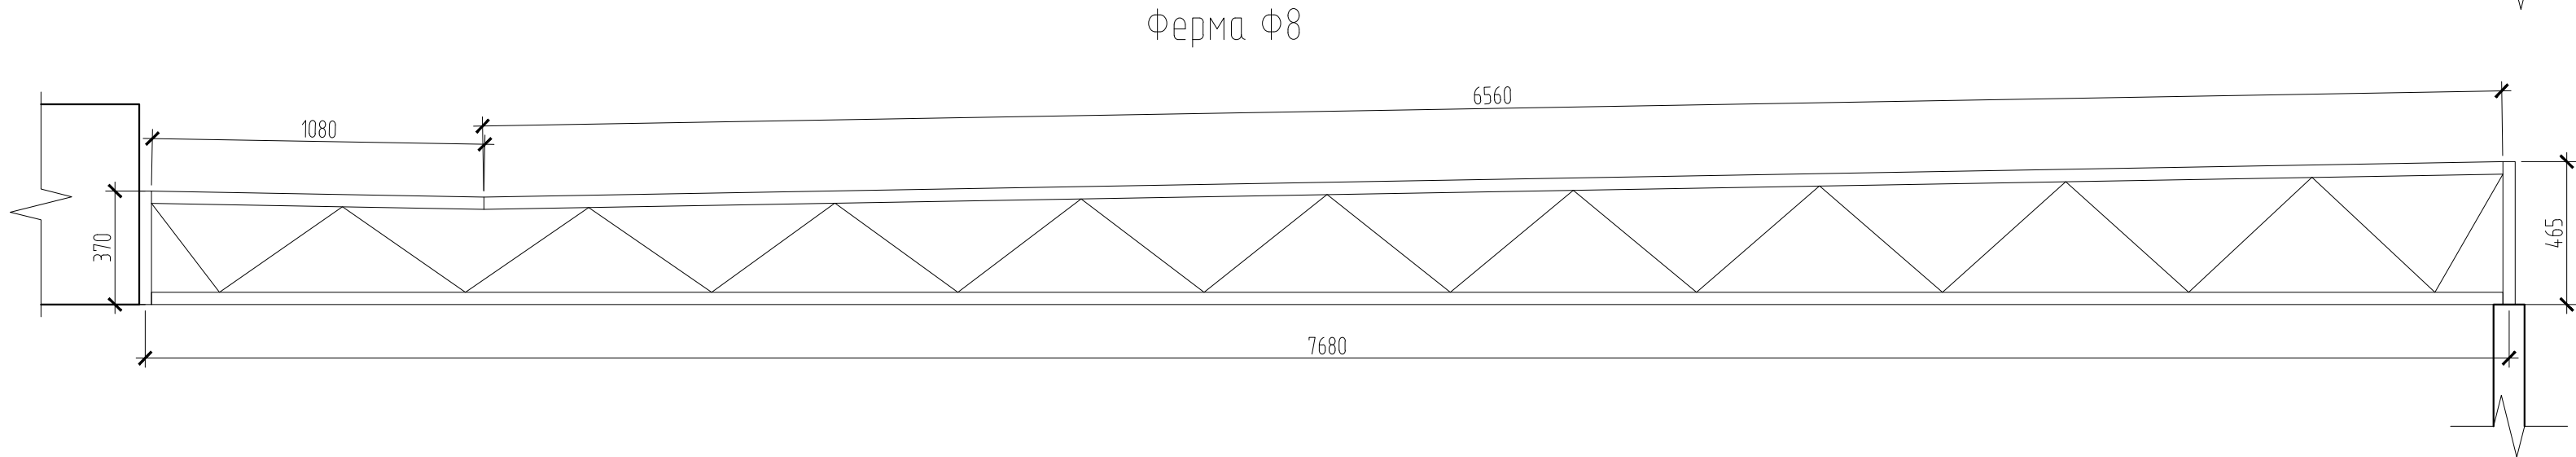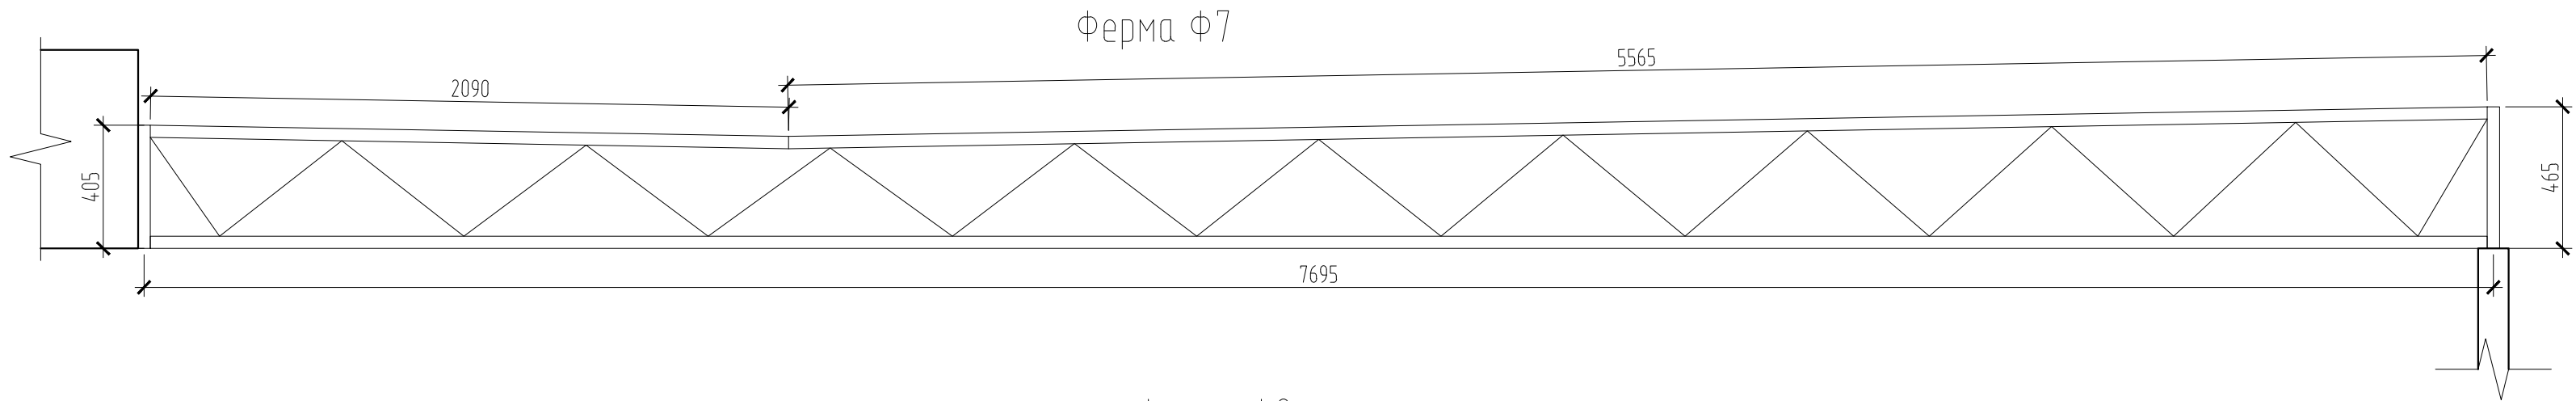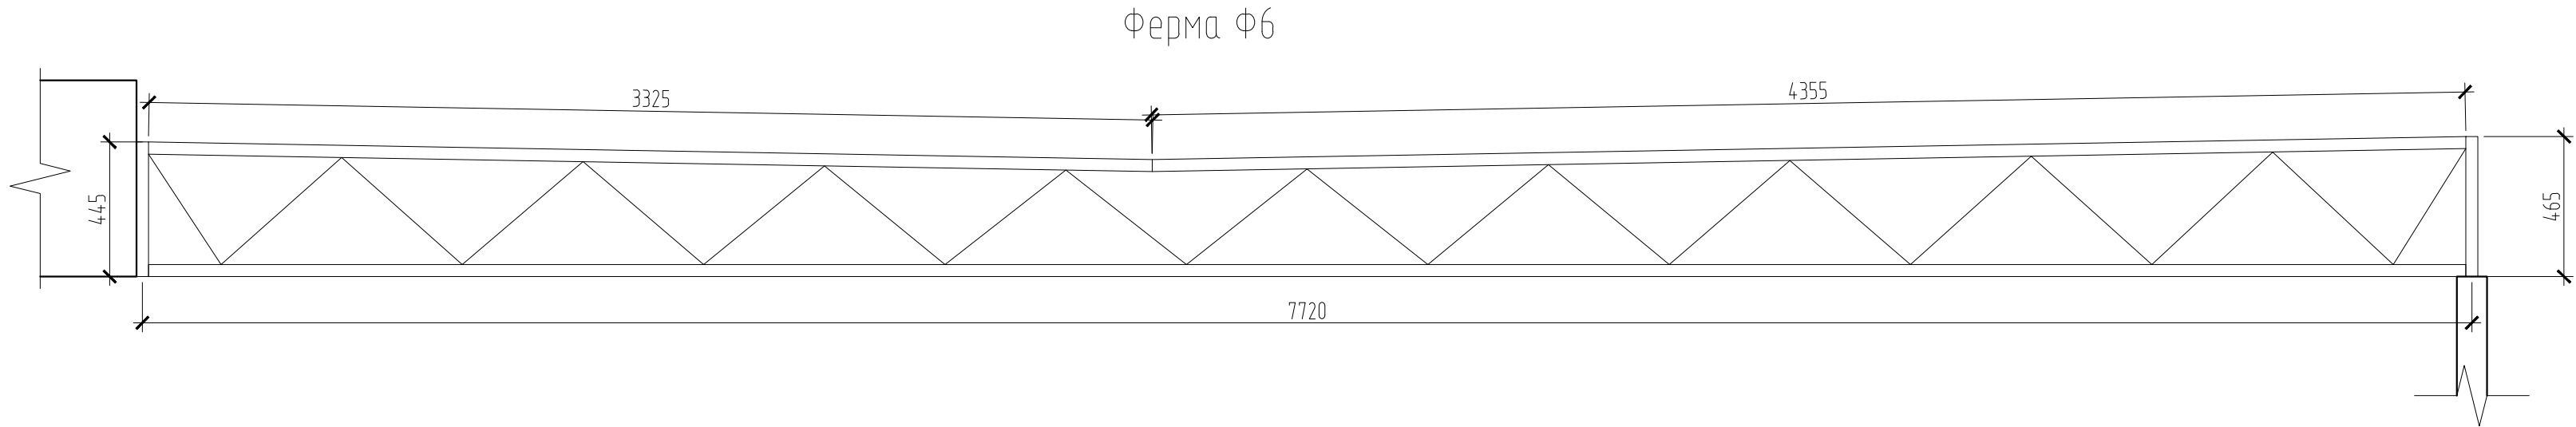

						1			
						1			
Изм.	Кол.уч.	Лист	№ док.	Подп.	Дата	1	Стадия	Лист	Листов
Разработал					05.24		Р	5	
ГИП					05.24				
							Фермы Ф6, Ф7, Ф8		
Н.контроль					05.24	1			






Согласовано:				
Взам. инб. №				
Подп. и дата				
Инб. № подл.				

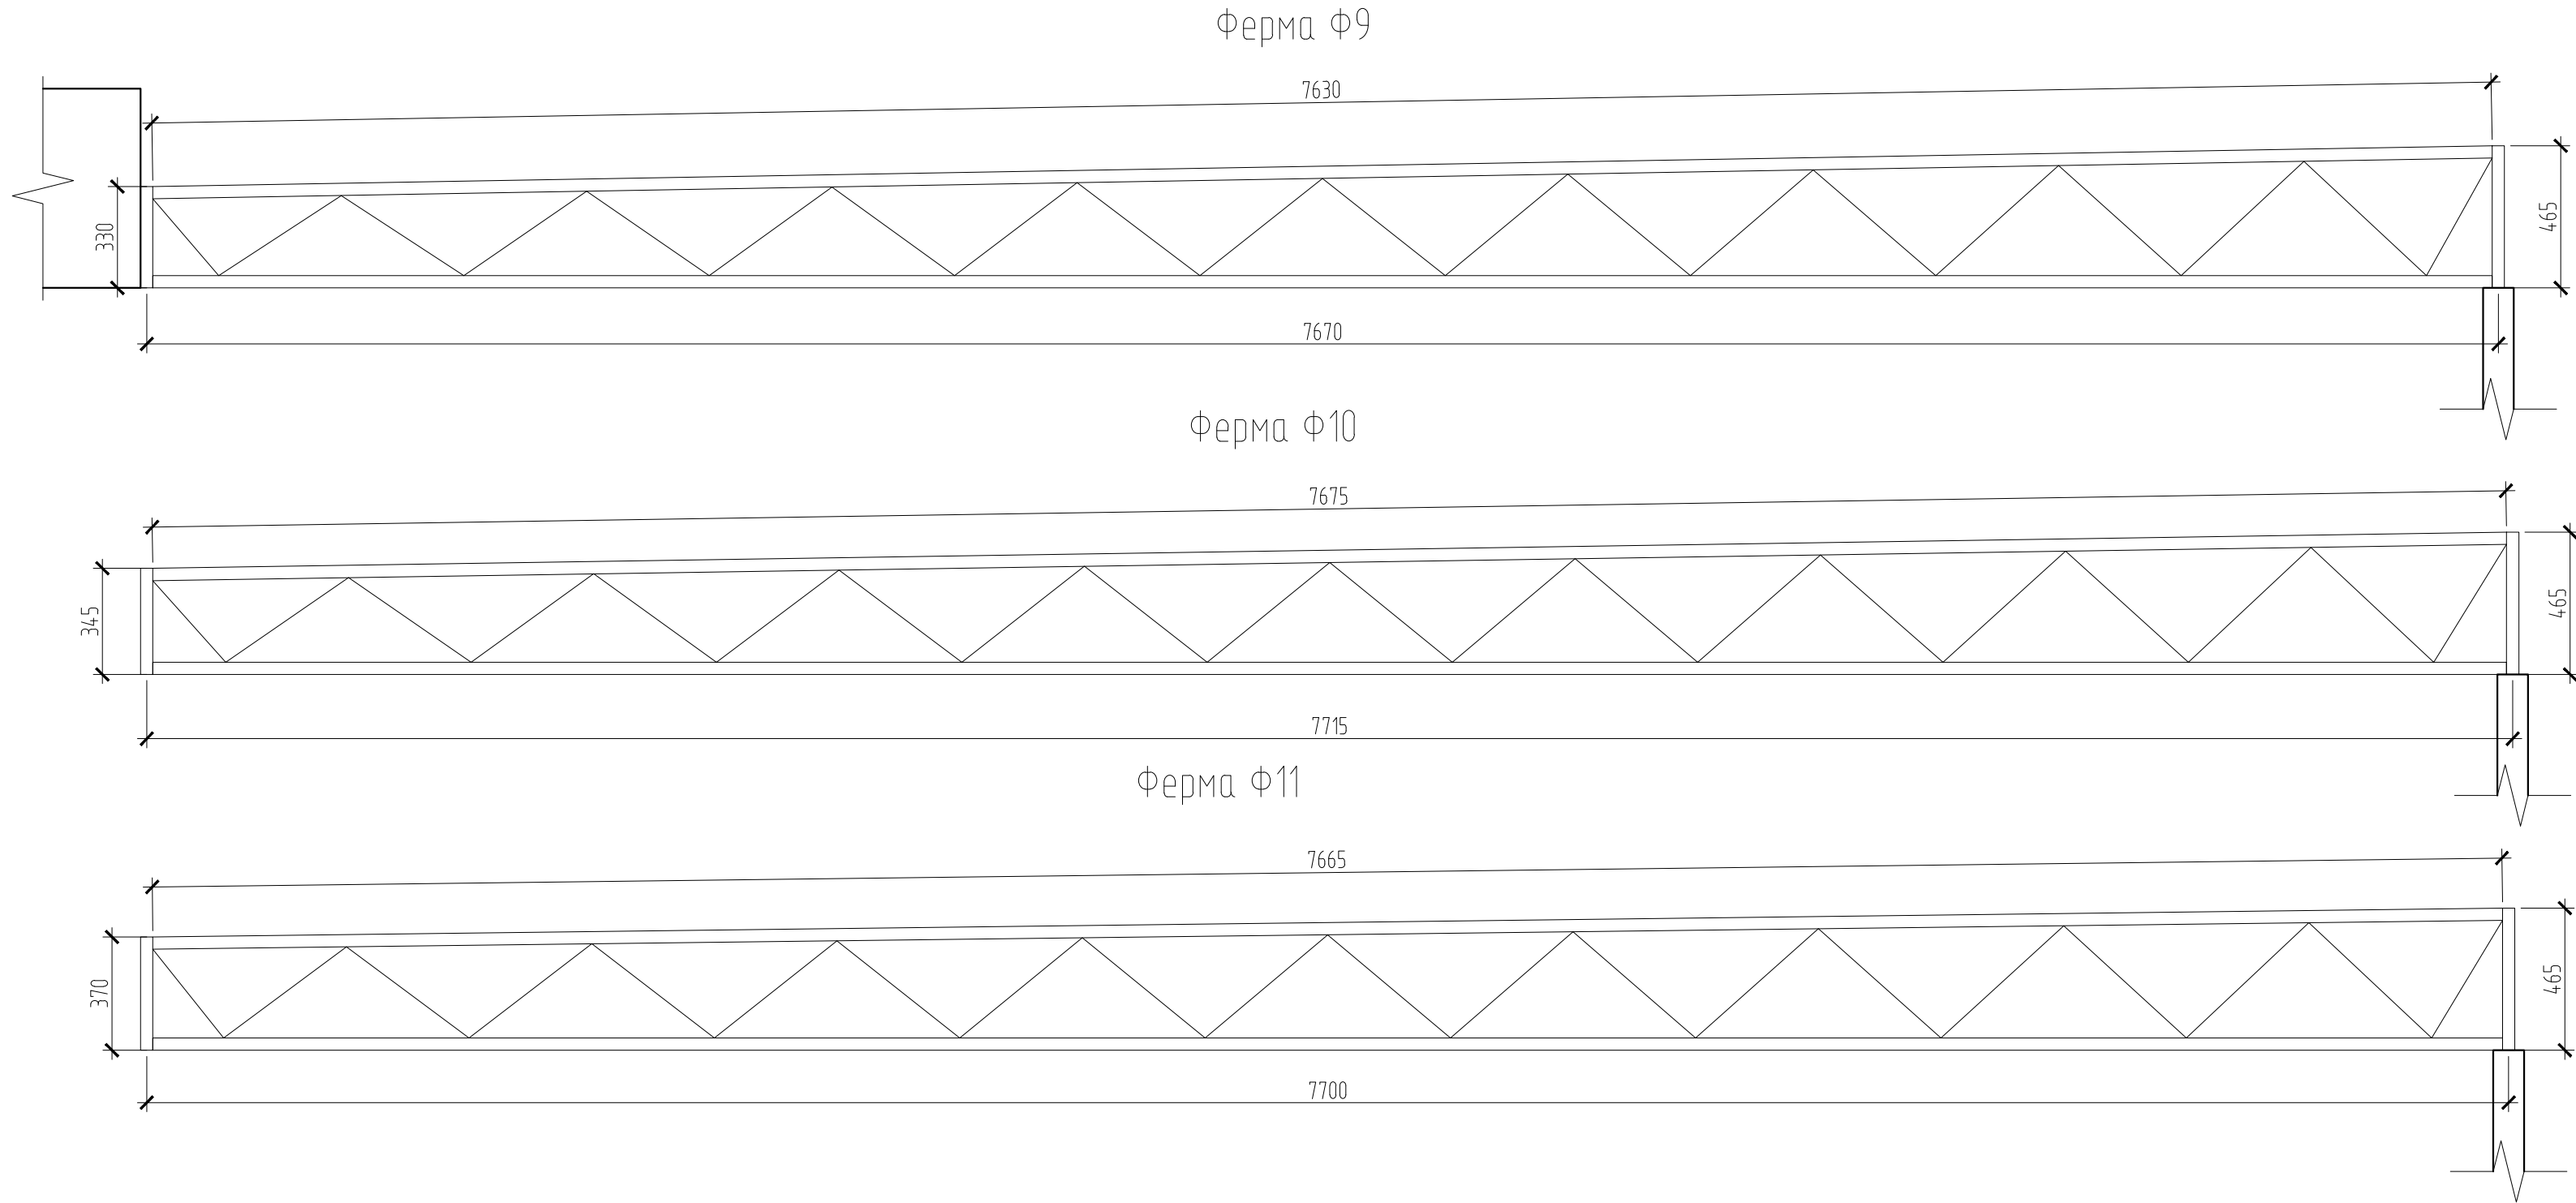

						1
						1
Изм.	Кол.уч.	Лист	№ док.	Подп.	Дата	
Разработал					05.24	
ГИП					05.24	1
Н.контроль					05.24	Фермы Ф9, Ф10, Ф11

Стадия	Лист	Листов
Р	6	
1		


Инф. № подл.	Подп. и дата	Взам. инв. №	Составлено:		

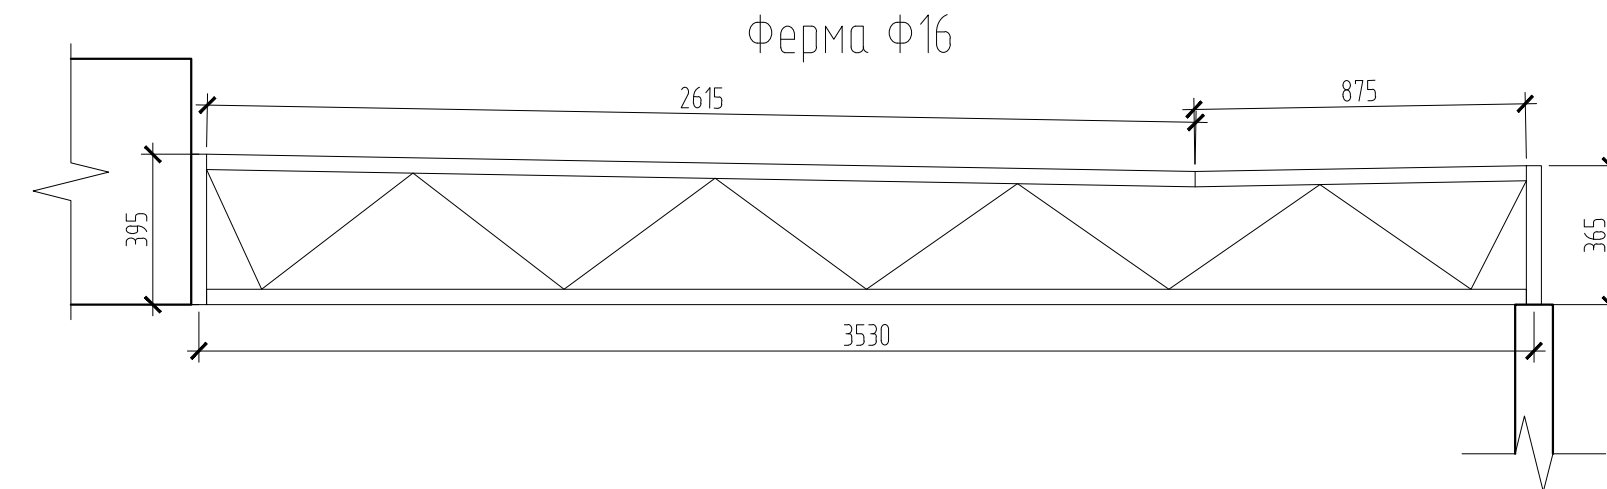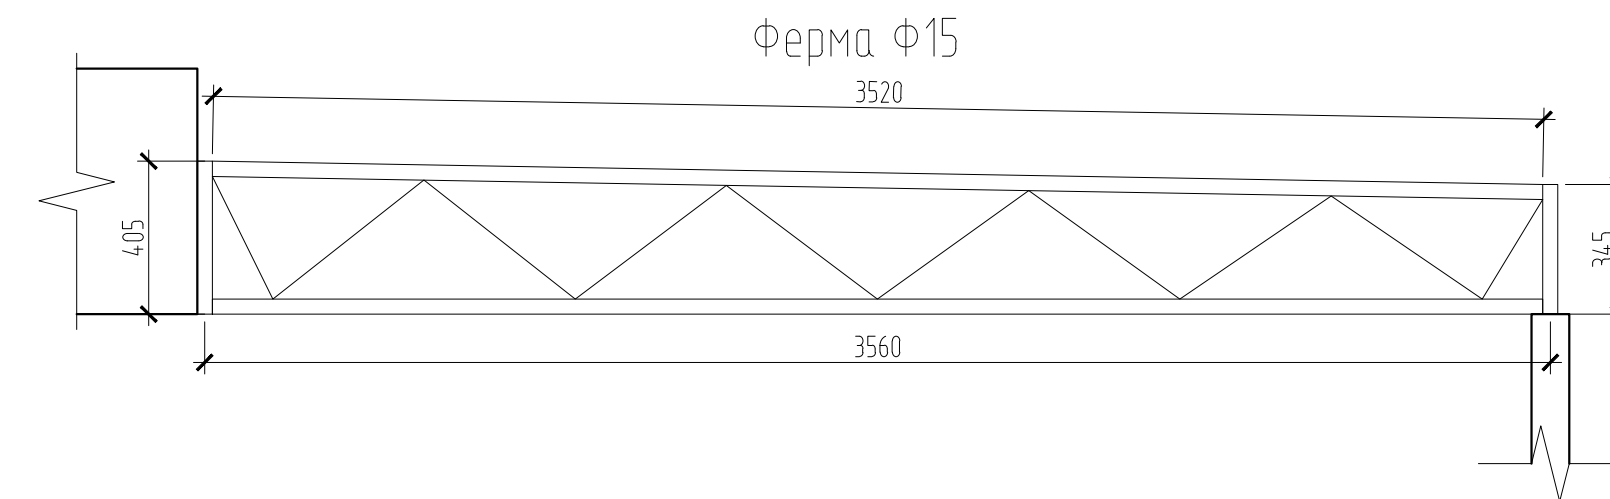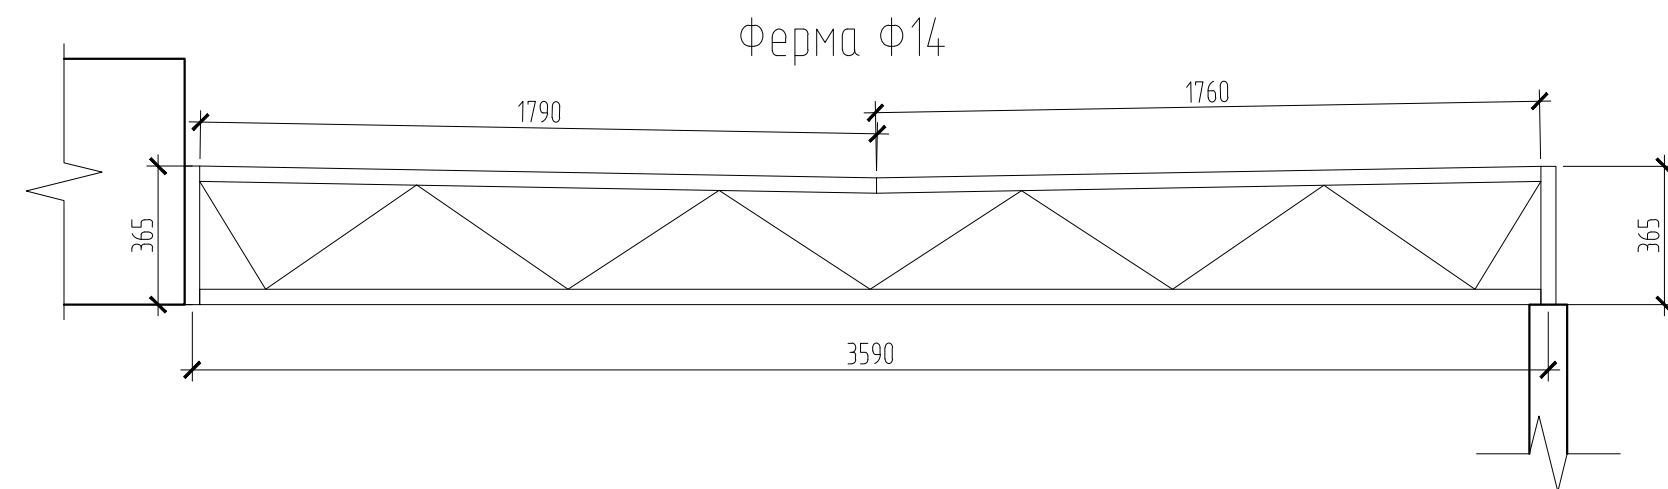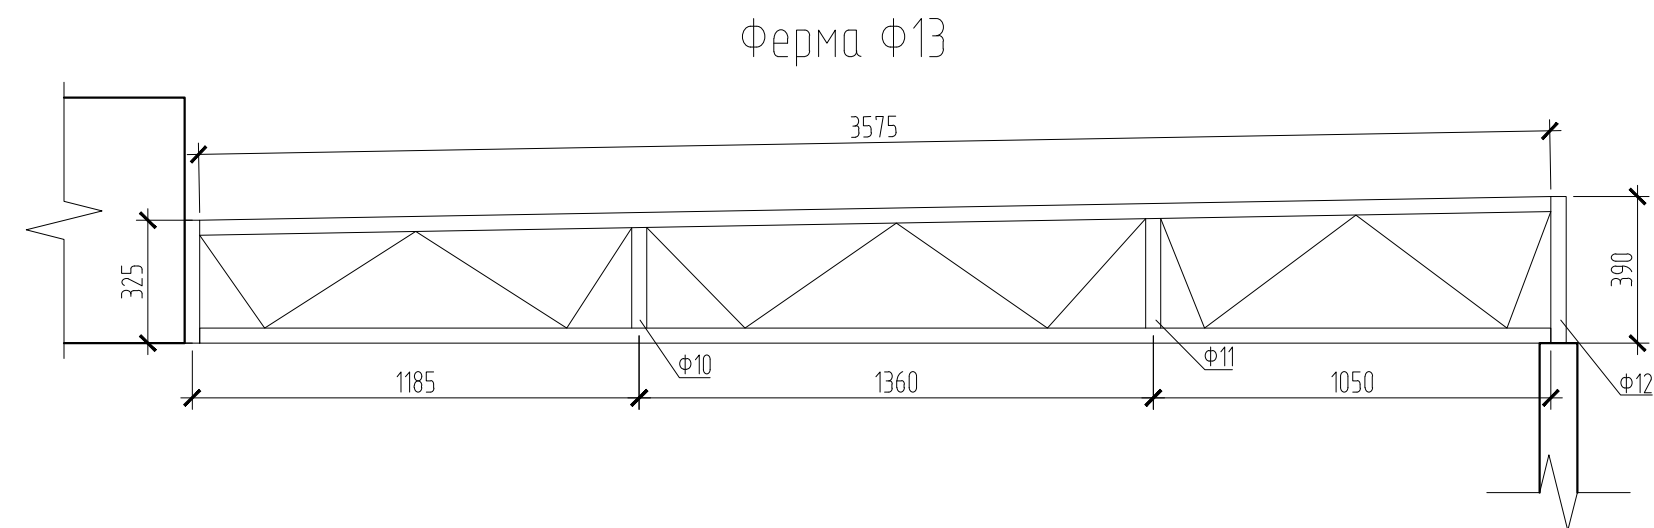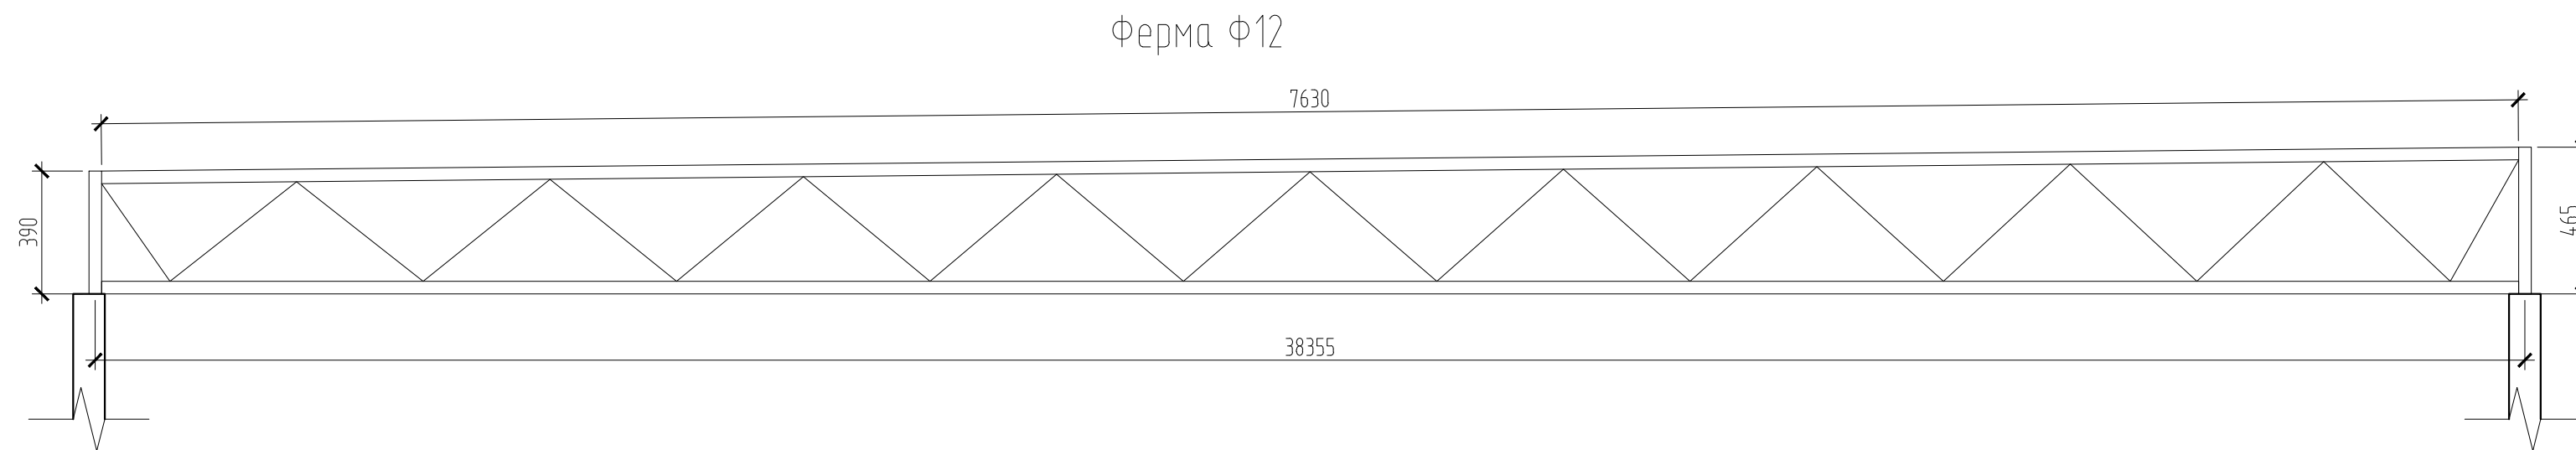

						1				
						1				
Изм.	Кол.уч	Лист	№ док	Подп.	Дата					
Разработал					05.24	1		Стадия	Лист	Листов
ГИП					05.24			Р	7	
						Фермы Ф12, ..., Ф16		1		
Н.контроль					05.24					

Согласовано:


Взам. инв. №
Подп. и дата
Инв. № подл.

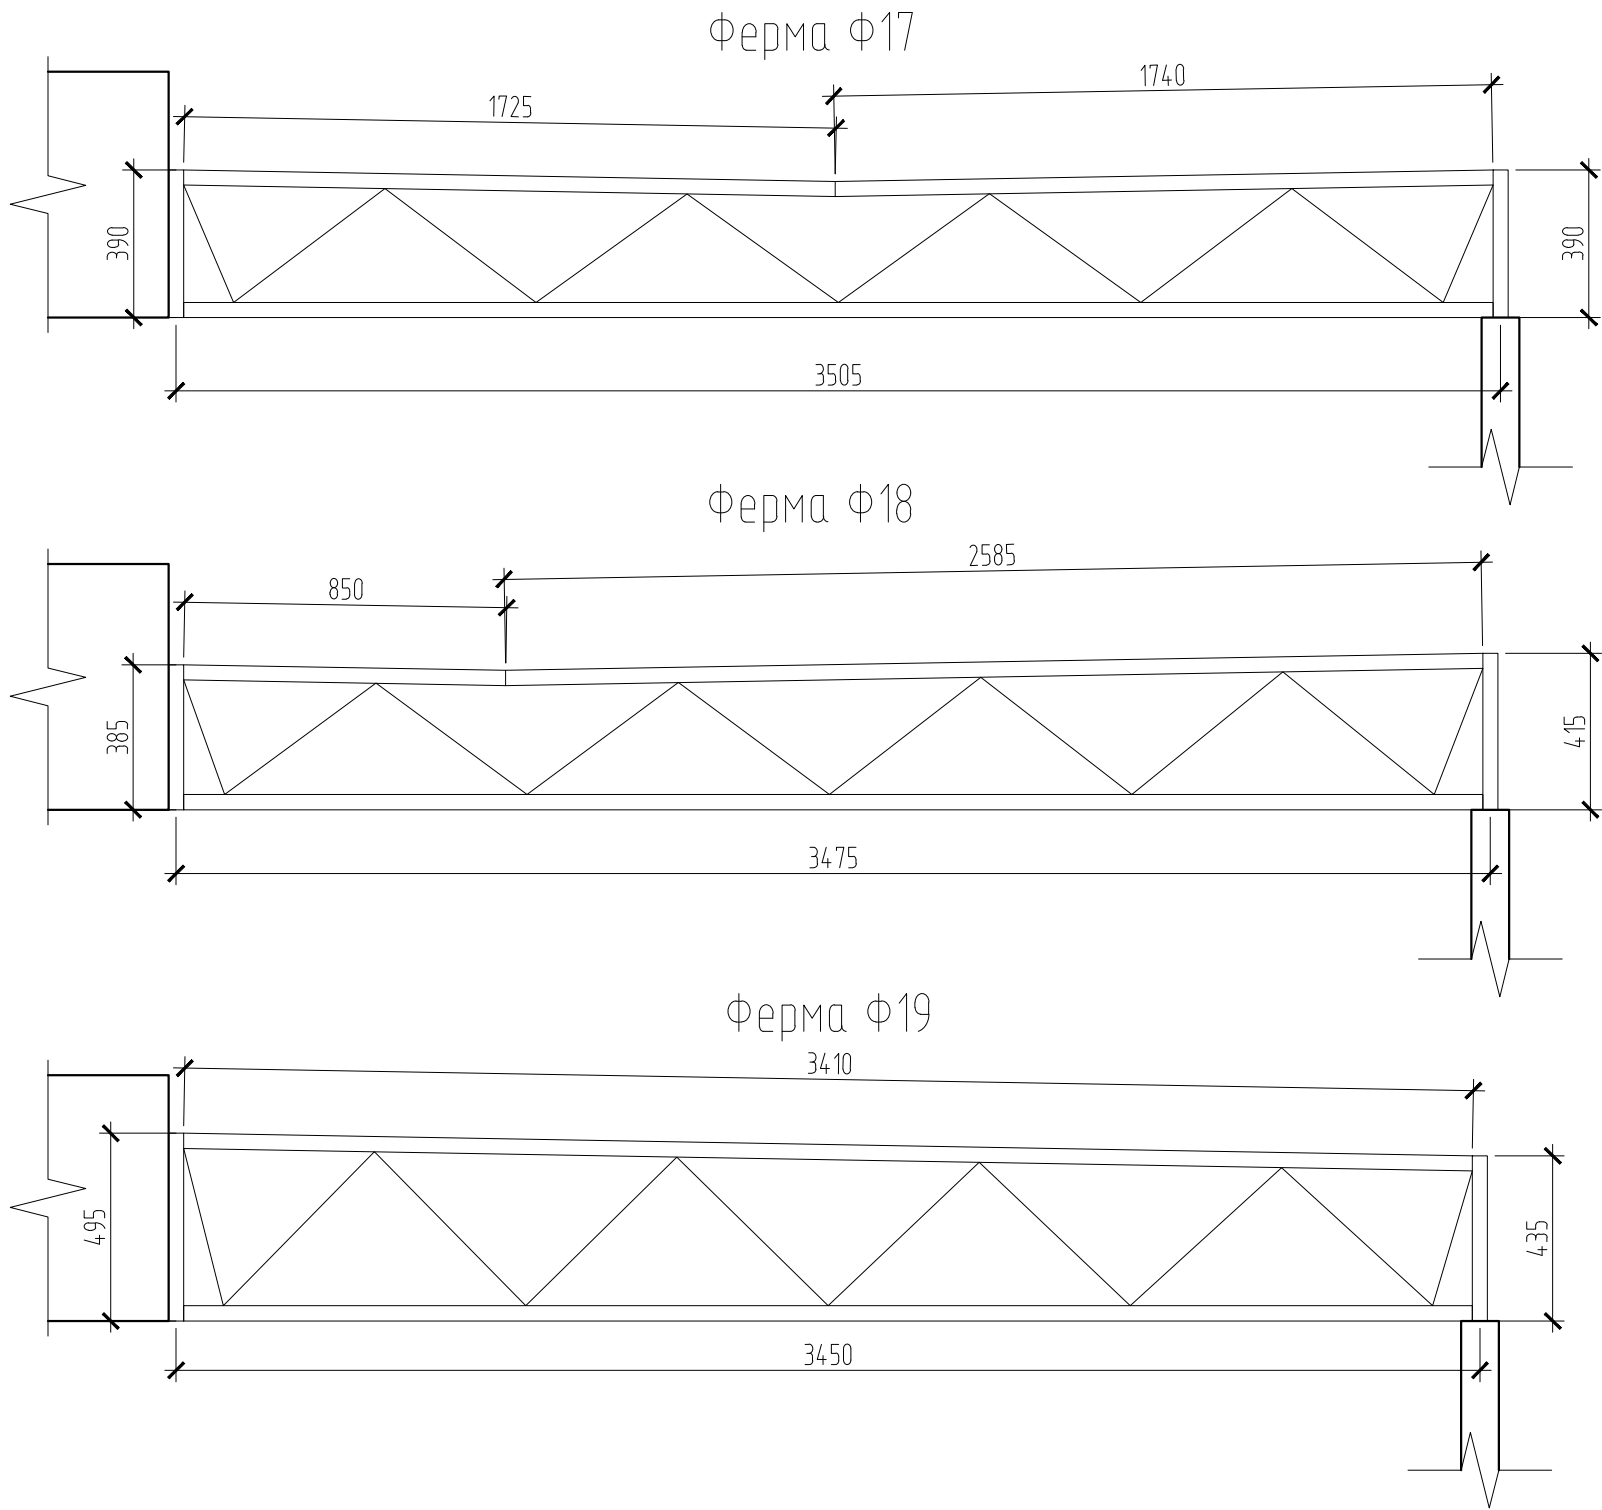


						1			
						1			
Изм.	Кол.уч.	Лист	№ док.	Подп.	Дата	1	Стадия	Лист	Листов
Разработал					05.24		Р	8	
ГИП					05.24				
						Фермы Ф17, Ф18, Ф19	1		
Н.контроль					05.24				

Согласовано:			
Взам. инв. №			
Подп. и дата			
Инв. № подл.			

Ферма Ф20

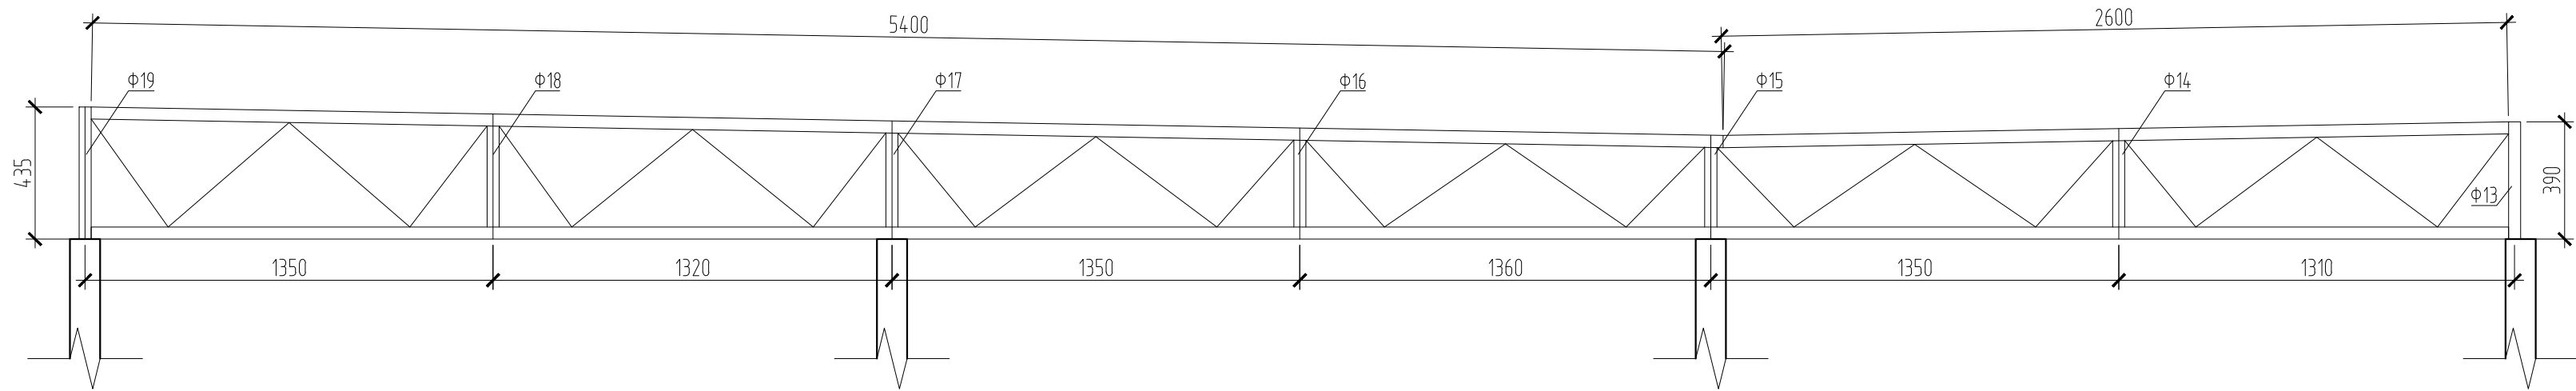

Ферма Ф21

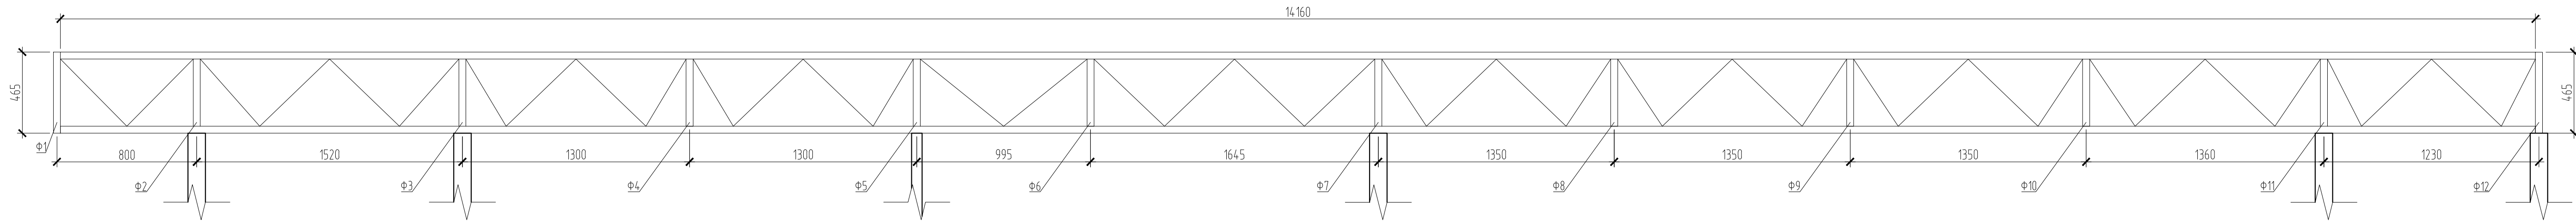

							1
							1
Изм.	Кол.уч.	Лист	№ док.	Подп.	Дата		
Разработал					05.24	1	Стадия
ГИП					05.24		Лист
							Р
							9
Н.контроль					05.24	Фермы Ф20, Ф21	1